

SUBSURFACE WASTEWATER DISPOSAL SYSTEM APPLICATION

Maine DHHS/CDC - Division of Environmental and Community Health
(207) 287-2070 | Fax (207) 287-4172 | subsurface.wastewater@maine.gov

Owner

KRISTEN MARQUIS


Address

17 ASPEN WAY

Scale: 1"= 100 ft.

SITE PLAN

SITE LOCATION

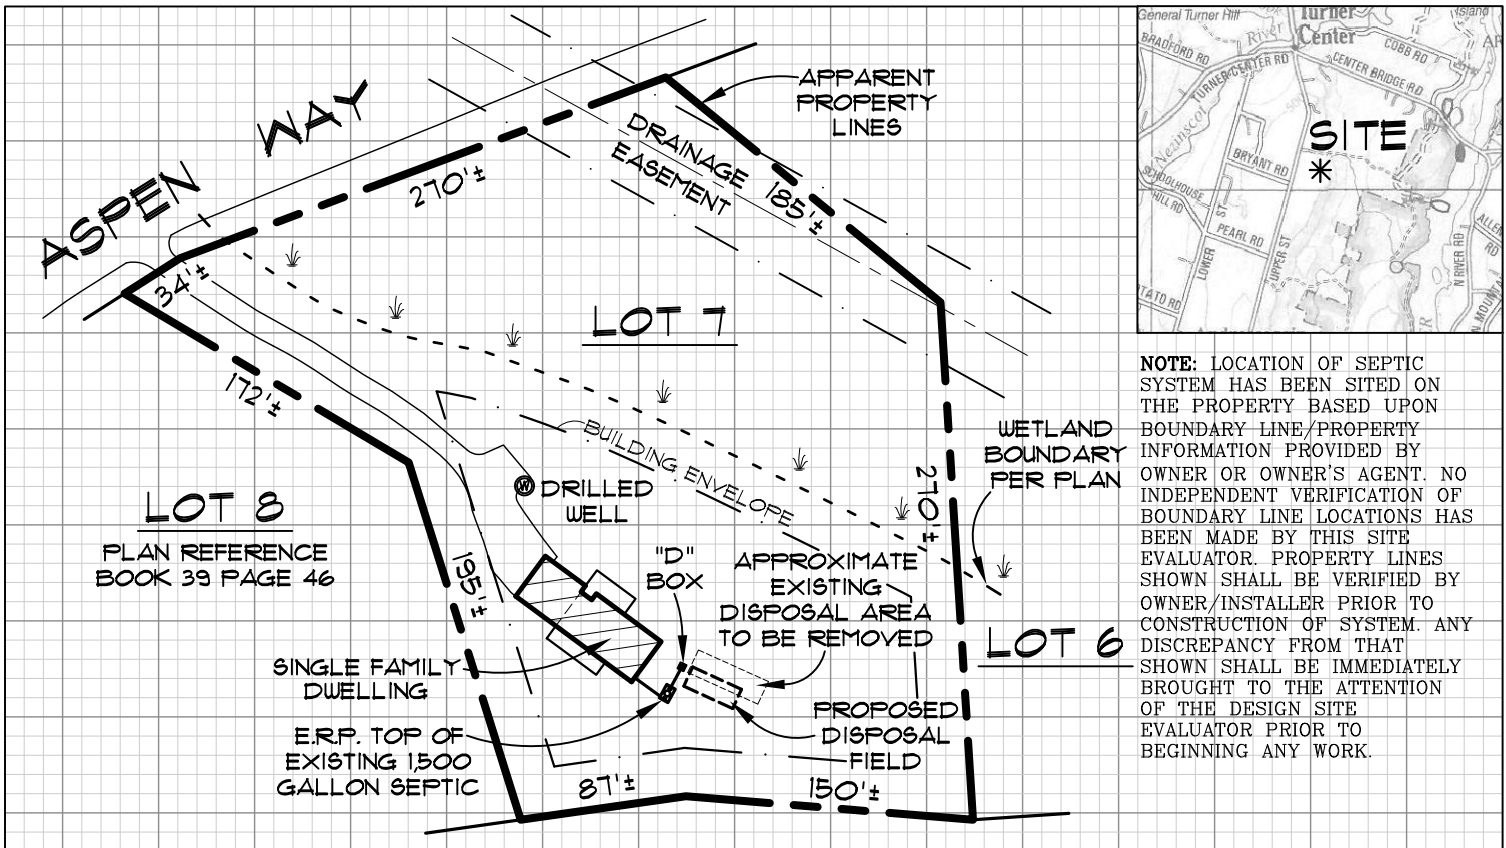

SOIL PROFILE DESCRIPTION AND CLASSIFICATION

(Location of Observation Holes Shown Above)

Observation Hole # Organic Horizon Thickness "
Test Pit ☐ Boring ☒ Ground Surface Elevation "
Depth to Exploration or Refusal "

Observation Hole # Organic Horizon Thickness "
Test Pit ☐ Boring ☐ Ground Surface Elevation "
Depth to Exploration or Refusal "

Textures	Consistency	Color	Redox Features
		BROWN	
FINE			
	FRIABLE		
		YELLOWISH	
SANDY			
		BROWN	
LOAM			
		LIGHT	
	FIRM	OLIVE	
		GRAY	

Textures	Consistency	Color	Redox Features
SPECIAL NOTE: EXISTING DISPOSAL FIELD, EXISTING BIOMATT AND A MINIMUM OF 12 INCHES OF EXISTING SOIL BELOW PROPOSED DISPOSAL AREA AND FILL EXTENSIONS SHALL BE REMOVED, WHERE ENCOUNTERED, AND REPLACED WITH SUITABLE SOIL BACKFILL PER SECTION 11(E) OF THE CODE.			

Geary Baerhle

338

2/19/2026

Site Evaluator Signature or Initials

SE #

Date