

SUBSURFACE WASTEWATER DISPOSAL SYSTEM APPLICATION

Maine DHHS/CDC - Division of Environmental and Community Health
(207) 287-2070 | Fax (207) 287-4172 | subsurface.wastewater@maine.gov

Owner


CHARLES ROBERTS

Address

450 LANE ROAD

Scale: 1"= 10 ft.

SUBSURFACE WASTEWATER DISPOSAL PLAN

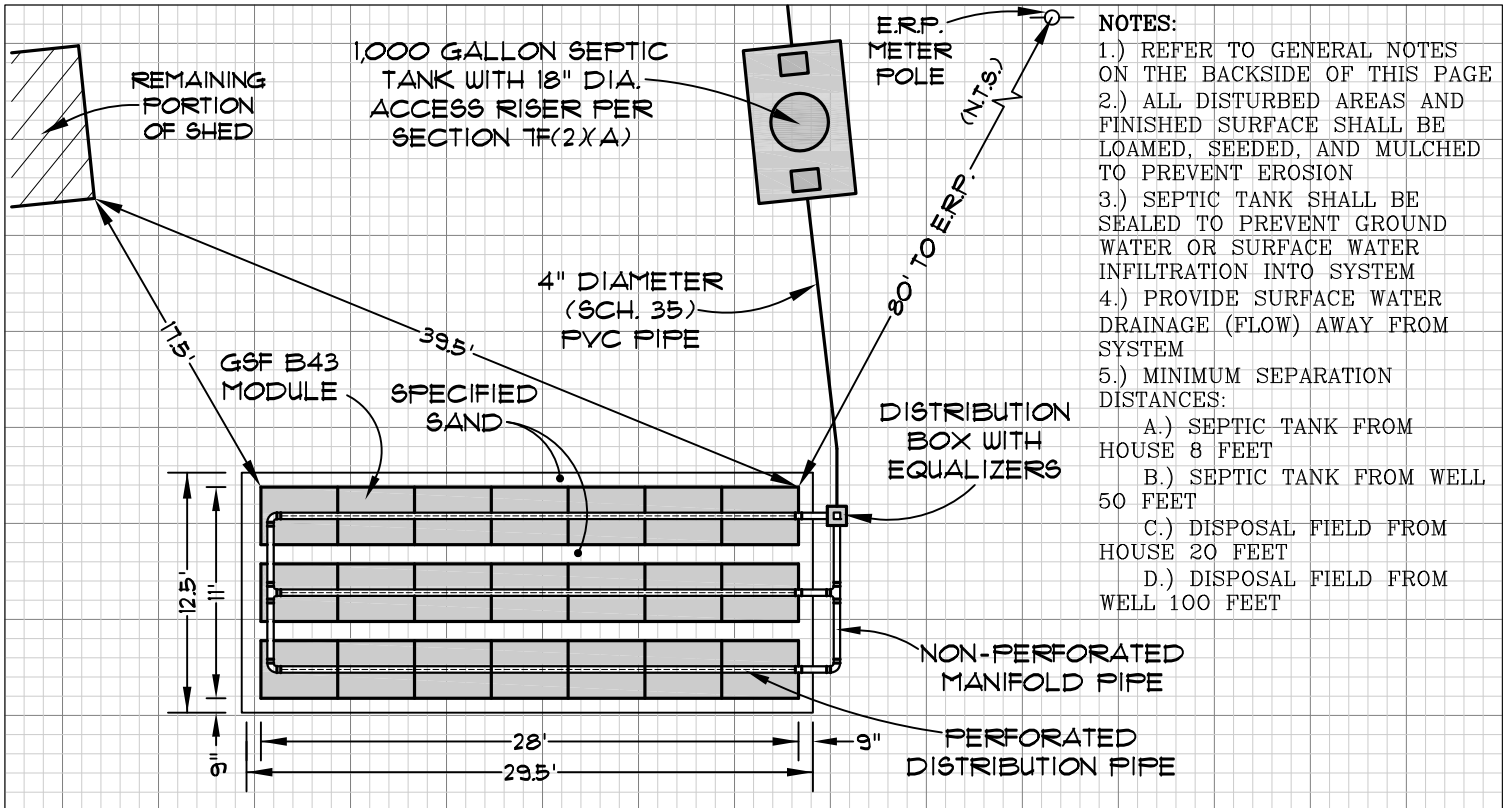

Backfill Requirements Above Existing Grade

Construction Elevations from Elevation Reference Point

Elevation Reference Point


Depth of Backfill (upslope)	4 "
Depth of Backfill (downslope)	10 "
Depths at Cross-Section (shown below)	

Finish Grade (Elevation)	-32 "
Top of Distribution Pipe or Proprietary Device	-44 "
Bottom of Disposal Field	-56 "

Location & Description: NAIL SET 33"
ABOVE GRADE IN METER POLE
Reference Elevation is: 0.0" or 0 "

Scales:
Vertical: 1"= 2.5 ft.
Horizontal: 1"= 5 ft.

DISPOSAL AREA CROSS-SECTION

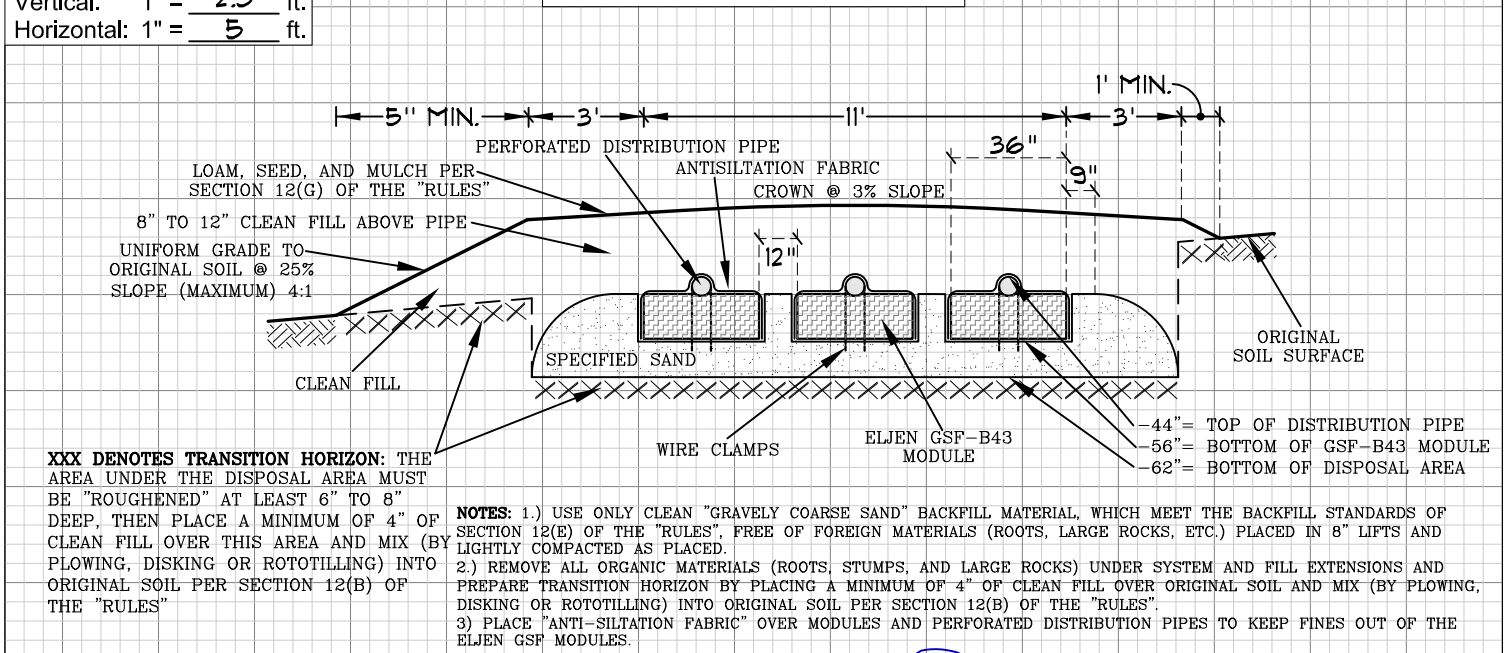

Geary D. Burch

Site Evaluator Signature or Initials

338

SE #

6/11/2026

Date