

SUBSURFACE WASTEWATER DISPOSAL SYSTEM PERMIT APPLICATION

Maine CDC: Drinking Water Program
Attn: SSWW Unit
286 Water Street, 3rd floor
Augusta, ME 04330

Property Address			
Address (# & Street)			
City/Town/ Plantation			
Municipal Tax Map #		Lot #	

Property Owner or Applicant Information	
Owner Name (Last, First)	
Applicant Name	

Owner or Applicant Mailing Address			
Street			
City		State	Zip
Phone			
Email			

Owner/ Applicant Statement	
I certify that the information submitted is correct to the best of my knowledge and understand that any falsification is reason for the Department and/or Local Plumbing Inspector(s) to deny a permit.	
X	
Property Owner/ Applicant Signature	Date

Installer Information	
Name	Phone
Email	

Issuing Municipality or Territory	
Permit #	Date Issued
X	

Local Plumbing Inspector Signature LPI #

A subsurface wastewater disposal system may not be installed until a permit is issued by the Local Plumbing Inspector. The permit authorizes the installation of the disposal system in accordance with 10-144-CMR Chapter 241.

CAUTION: INSPECTION REQUIRED

"I have inspected the installation authorized above and found it to be in compliance with the Subsurface Wastewater Disposal Rules Application."

X	
---	--

Local Plumbing Inspector Signature Date

X	
---	--

Local Plumbing Inspector Signature Date

Fee Calculations (For Town/ LPI Use Only)	
☐ Revision	
☐ Doubled Fee	
☐ Variance	
☐ Seas. Conv.	
Total Fee	\$
Town Share	\$
State 25%	\$
DEP WQS	\$
The Town retains all doubled fees The State receives 25% for First-time variances requiring State approval <i>only</i> Seas. Conv. must be a stand-alone permit	

Type of Application	Variance Requirements
☐ 1. First Time System	☐ 1. No Rule Variance
☐ 2. Replacement System	☐ 2. First Time System
Type Replaced	LPI Only ☐
Year Installed	State Required ☐
☐ 3. Expansion	☐ 3. Replacement System
☐ <25% (Minor) Expansion	LPI Only ☐
☐ ≥25% (Major) Expansion	State Required ☐
☐ 4. Experimental System	☐ 4. Minimum Lot Size
☐ 5. Seasonal Conversion Permit	☐ 5. Seasonal Conversion
Treatment Tank(s)	
☐ 1. Concrete	☐ Regular ☐ Low Profile ☐ H-20
☐ 2. Plastic	
☐ 3. External Grease Interceptor	Capacity
☐ 4. Other	Specify
Tank Capacity	gals
Total # of New Tanks	
Notes:	
☐ Riser(s) required in accordance with 10-144-CMR Chapter 241 (7)(F)(2)(a)	

Disposal System Components	
☐ 1. Complete Non-Engineered System	(Field /Tank /Pump)
Specify Total Number of New Tanks	
☐ 2. Primitive/ Limited System (Greywater + Alternative Toilet)	
Specify Type	
☐ 3. Alternative Toilet	
Specify Type	
☐ 4. Non-Engineered Treatment Tank(s)	(750 gals or over*)
Specify Total # of New Tanks:	
☐ 5. Holding Tank	
☐ 6. Non-Engineered Disposal Field	
☐ 7. Complete Engineered System	(Field/ 2 Tanks/ Pump)
New: # Disposal Fields # Tanks # Pumps	
☐ 8. Engineered Tank(s) Only	Specify # of New Tanks
☐ 9. Engineered Field(s) Only	
☐ 10. Miscellaneous Components	Specify
☐ 11. Pre-Treatment Tank (Tank fees apply)**	
☐ 12. Pre-Treatment Component (Misc. Component fees apply)**	
*Includes Grease Interceptors, Pump Tanks, etc. **Details on Pg. 2	

Site Evaluator Statement

I certify that I have completed a site evaluation on this property and state that the data reported are accurate and that the proposed system is in compliance with the State of Maine Subsurface Wastewater Disposal Rules (10-144A CMR 241).

Site Evaluator Name (Print)		Phone		SE #	
Signature		Date		Email	

SUBSURFACE WASTEWATER DISPOSAL SYSTEM APPLICATIONMaine DHHS/CDC – Division of Environmental and Community Health
(207) 287-2070 | Fax (207) 287-4172 | subsurface.wastewater@maine.gov

Owner

Address

Property Size ☐ sq. ft. ☐ acres**Shoreland Zoning**☐ Yes**Current Use**☐ Seasonal ☐ Undeveloped
☐ No ☐ Year-Round ☐ Commercial**Latitude & Longitude (D.M.S.)**Latitude
Longitude

GPS margin of error

Type of Water Supply☐ 1. Drilled Well ☐ 2. Dug/ Point Well
☐ 3. Private ☐ 4. Public ☐ 5. Other

Specify:

Effluent/ Ejector PumpRequired: ☐ Yes ☐ No ☐ MaybeDose (Engineered Systems) gals**Garbage Disposal Unit**☐ Yes ☐ No ☐ Maybe *If Yes...*☐ Multi-compartment Tank
☐ Tanks in Series # of Tanks
☐ Increase Tank Capacity
☐ Filter on Tank Outlet**Pre-/ Advanced Treatment Systems**

Make

Model

Notes:

☐ Maintenance contract (HHE-300A) required

Make

Model

Notes:

☐ Maintenance contract (HHE-300A) required**Disposal System to Serve**☐ 1. Single Family Dwelling Unit# of bedrooms: ☐ 2. Multiple Family Dwelling Units# of bedrooms: ☐ 3. Accessory Dwelling Unit(s)# of bedrooms: ☐ 4. Other

Specify:

Disposal Field Type & Size☐ 1. Stone Bed
☐ 2. Stone Trench
☐ 3. Proprietary Device
☐ Cluster Array ☐ Linear
☐ Regular ☐ Load
☐ 4. Other

Specify:

Size ☐ sq. ft. ☐ lin. ft.**Design Flow** Gallons per Day

Based on (select one)

☐ 1. Table 5A (Dwelling Units)
☐ 2. Table 5C (Other Facilities)

Show Calculations for "Other Facilities"

☐ 3. Section 5(G) – Meter Readings

ATTACH WATER METER DATA

Soil Data & Design Class

Profile

Condition

At Observation Hole #

Limiting Factor Depth

Limiting Factor Elevation

Highest Elevation within Disposal Field

Additional Notes

Site Evaluator Signature or Initials

SE #


Date

SUBSURFACE WASTEWATER DISPOSAL SYSTEM APPLICATION

Owner
Kristen Marquis
Address

Scale 1" = 100 ft

SITE PLAN

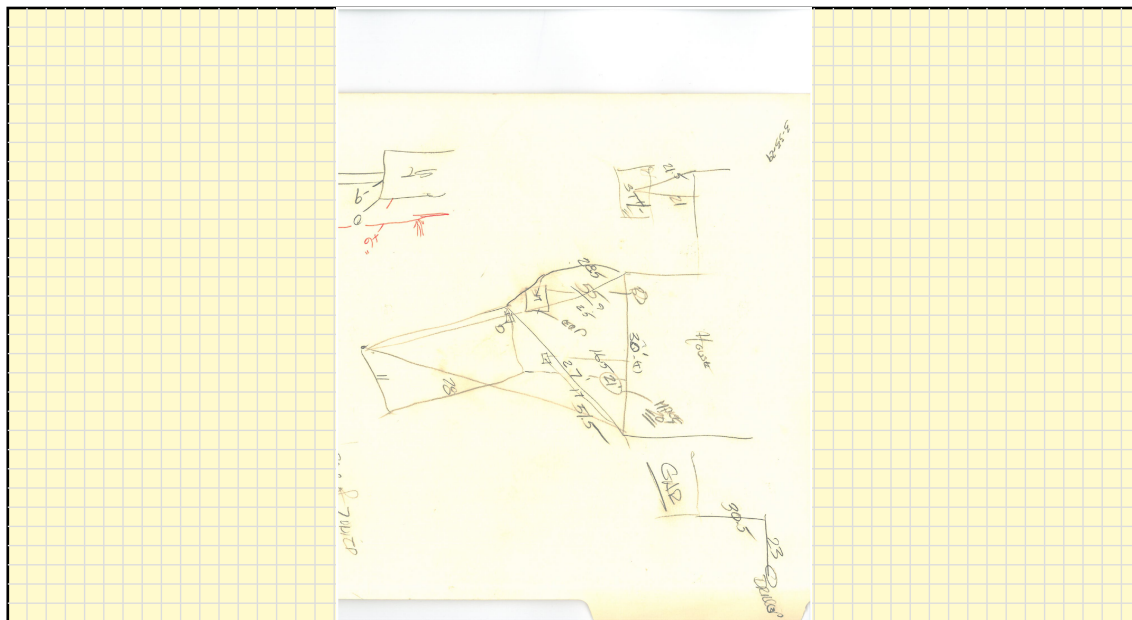

SITE LOCATION

*

NOTE: LOCATION OF SEPTIC SYSTEM HAS BEEN SITED ON THE PROPERTY BASED UPON BOUNDARY LINE/PROPERTY INFORMATION PROVIDED BY OWNER OR OWNER'S AGENT. NO INDEPENDENT VERIFICATION OF BOUNDARY LINE LOCATIONS HAS BEEN MADE BY THIS SITE EVALUATOR. PROFESSIONAL BOUNDARY SURVEYS HAVE BEEN VERIFIED BY OWNER/INSTALLER PRIOR TO SYSTEM INSTALLATION. ANY DISCREPANCY FROM THAT SHOWN SHALL BE IMMEDIATELY BROUGHT TO THE ATTENTION OF THE DESIGN SITE EVALUATOR PRIOR TO BEGINNING ANY WORK.

SOIL PROFILE DESCRIPTION AND CLASSIFICATION

Depth	Obs #	Textures	Consistency	Color	Redox
48"					
42"					
36"					
30"					
24"					
18"					
12"					
6"					

Location of Observation Holes Shown Above

Site Evaluator Signature or Initials

SE #


Date

SUBSURFACE WASTEWATER DISPOSAL SYSTEM APPLICATION

Owner
Kristen Marquis
Address

Top Scale 1" = 10 ft


SUBSURFACE WASTEWATER DISPOSAL PLAN

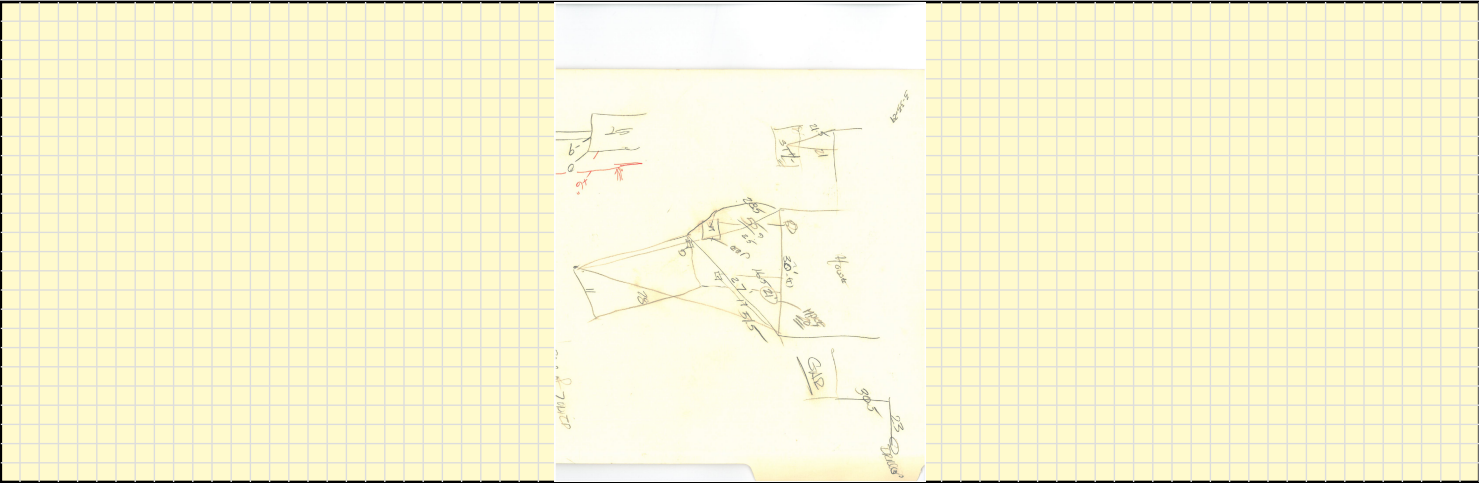

TANK / DISTRIBUTION BOX		
Type	Capacity	Elevation
Concrete	1000 gal	TBD

PIPE SPECS	
Size	Slope
4"	1/8"

NOTES AND SPECIFICATIONS

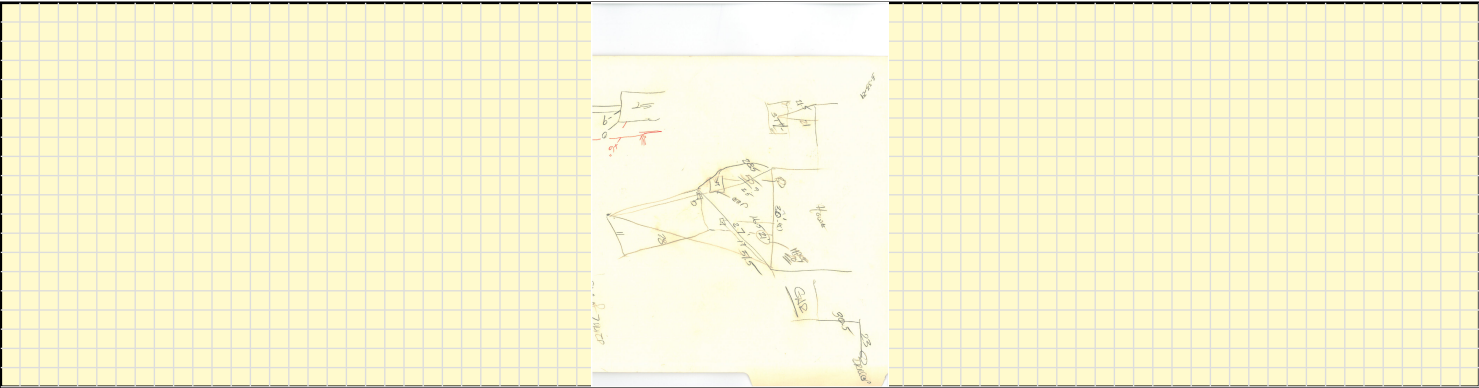

SYSTEM NOTES

GSF-B43 Module approved for this application. System designed per Maine Department of Health & Human Services standards.

All work shall be in accordance with the approved

Site Evaluator Signature or Initials

SE #

Date