

SUBSURFACE WASTEWATER DISPOSAL SYSTEM PERMIT APPLICATION

Maine CDC: Drinking Water Program
Attn: SSWW Unit
286 Water Street, 3rd floor
Augusta, ME 04330

Property Address			
Address (# & Street)	17	Aspen Way	
City/Town/ Plantation	Turner		
Municipal Tax Map #	26	Lot #	18

Property Owner or Applicant Information	
Owner Name (Last, First)	Kristen Marquis
Applicant Name	Kristen Marquis

Owner or Applicant Mailing Address			
Street			
City	Turner	State	Maine
Zip	04282		
Phone			
Email			

Owner/ Applicant Statement	
I certify that the information submitted is correct to the best of my knowledge and understand that any falsification is reason for the Department and/or Local Plumbing Inspector(s) to deny a permit.	
X	3/1/2026
Property Owner/ Applicant Signature	Date

Installer Information	
Name	
Phone	
Email	

Issuing Municipality or Territory	
Permit #	
Date Issued	
X	338

Local Plumbing Inspector Signature

LPI #

A subsurface wastewater disposal system may not be installed until a permit is issued by the Local Plumbing Inspector. The permit authorizes the installation of the disposal system in accordance with 10-144-CMR Chapter 241.

CAUTION: INSPECTION REQUIRED

"I have inspected the installation authorized above and found it to be in compliance with the Subsurface Wastewater Disposal Rules Application."

X	
---	--

Local Plumbing Inspector Signature

Date

X	
---	--

Local Plumbing Inspector Signature

Date

Fee Calculations (For Town/ LPI Use Only)	
☐ Revision	
☐ Doubled Fee	
☐ Variance	
☐ Seas. Conv.	
Total Fee	\$
Town Share	\$
State 25%	\$
DEP WQS	\$

The Town retains all doubled fees
The State receives 25% for First-time variances requiring State approval *only*
Seas. Conv. must be a stand-alone permit

Type of Application	Variance Requirements
☐ 1. First Time System	☐ 1. No Rule Variance
☐ 2. Replacement System	☐ 2. First Time System
Type Replaced	LPI Only ☐
Year Installed	State Required ☐
☐ 3. Expansion	☐ 3. Replacement System
☐ <25% (Minor) Expansion	LPI Only ☐
☐ ≥25% (Major) Expansion	State Required ☐
☐ 4. Experimental System	☐ 4. Minimum Lot Size
☐ 5. Seasonal Conversion Permit	☐ 5. Seasonal Conversion
Treatment Tank(s)	
☐ 1. Concrete	☒ Regular
☐ 2. Plastic	☐ Low Profile
☐ 3. External Grease Interceptor	Capacity 1,000 gals
☐ 4. Other	Specify
Tank Capacity 1,000 gals	Total # of New Tanks
Notes:	
☐ Riser(s) required in accordance with 10-144-CMR Chapter 241 (7)(F)(2)(a)	

Disposal System Components	
☐ 1. Complete Non-Engineered System	(Field /Tank /Pump)
Specify Total Number of New Tanks	
☐ 2. Primitive/ Limited System (Greywater + Alternative Toilet)	
Specify Type	
☐ 3. Alternative Toilet	
Specify Type	
☐ 4. Non-Engineered Treatment Tank(s)	(750 gals or over*)
Specify Total # of New Tanks:	
☐ 5. Holding Tank	
☒ 6. Non-Engineered Disposal Field	
☐ 7. Complete Engineered System	(Field/ 2 Tanks/ Pump)
New: # Disposal Fields # Tanks # Pumps	
☐ 8. Engineered Tank(s) Only	Specify # of New Tanks
☐ 9. Engineered Field(s) Only	
☐ 10. Miscellaneous Components	Specify
☐ 11. Pre-Treatment Tank (Tank fees apply)**	
☐ 12. Pre-Treatment Component (Misc. Component fees apply)**	
*Includes Grease Interceptors, Pump Tanks, etc. **Details on Pg. 2	

Site Evaluator Statement			
I certify that I have completed a site evaluation on this property and state that the data reported are accurate and that the proposed system is in compliance with the State of Maine Subsurface Wastewater Disposal Rules (10-144A CMR 241).			
Site Evaluator Name (Print)	George Bouchles	Phone	207-240-5567
SE #	338		
Signature		Date	3/1/2026
Email	gsb@cadmasterr.com		

SUBSURFACE WASTEWATER DISPOSAL SYSTEM APPLICATIONMaine DHHS/CDC – Division of Environmental and Community Health
(207) 287-2070 | Fax (207) 287-4172 | subsurface.wastewater@maine.gov

Owner Kristen Marquis

Address 17 Aspen Way, Turner, Maine 042

Property Size2.35 ☐ sq. ft. ☒ acres**Shoreland Zoning**☐ Yes**Current Use**☐ Seasonal ☐ Undeveloped
☐ No ☒ Year-Round ☐ Commercial**Latitude & Longitude (D.M.S.)**Latitude
Longitude

GPS margin of error 30

Type of Water Supply☒ 1. Drilled Well ☐ 2. Dug/ Point Well
☐ 3. Private ☐ 4. Public ☐ 5. Other

Specify: existing drilled well

Effluent/ Ejector PumpRequired: ☐ Yes ☐ No ☐ MaybeDose (Engineered Systems) gals**Garbage Disposal Unit**☐ Yes ☒ No ☐ Maybe If Yes...☐ Multi-compartment Tank☐ Tanks in Series # of Tanks 0☐ Increase Tank Capacity☐ Filter on Tank Outlet**Pre-/ Advanced Treatment Systems**Make Model

Notes:

☐ Maintenance contract (HHE-300A) requiredMake Model

Notes:

☐ Maintenance contract (HHE-300A) required**Disposal System to Serve**☒ 1. Single Family Dwelling Unit

of bedrooms: 3

☐ 2. Multiple Family Dwelling Units# of bedrooms: ☐ 3. Accessory Dwelling Unit(s)# of bedrooms: ☐ 4. Other

Specify:

Disposal Field Type & Size☐ 1. Stone Bed☐ 2. Stone Trench☒ 3. Proprietary Device☐ Cluster Array ☐ Linear
☐ Regular ☐ Load☐ 4. Other

Specify:

Size 3 rows ☒ sq. ft. ☐ lin. ft.**Design Flow**

270 Gallons per Day

Based on (select one)

☐ 1. Table 5A (Dwelling Units)☐ 2. Table 5C (Other Facilities)

Show Calculations for "Other Facilities"

☐ 3. Section 5(G) – Meter Readings

ATTACH WATER METER DATA

Soil Data & Design Class

Profile

Condition

At Observation Hole # OH-1, C

Limiting Factor Depth Ground Water

Limiting Factor Elevation 24 in

Highest Elevation within Disposal Field

Additional Notes

Septic tank: existing 1,000 gallon septic tank shall be exposed, inspected for structural integrity. if need, tank shall be replaced. outlet baffle shall be inspected and replaced if necessary.

338

3/1/2026

Site Evaluator Signature or Initials

SE #

Date

SUBSURFACE WASTEWATER DISPOSAL SYSTEM APPLICATION


Maine DHHS/CDC – Division of Environmental and Community Health
(207) 287-2070 | Fax (207) 287-4172 | subsurface.wastewater@maine.gov

Owner

Kristen Marquis

Address

17 Aspen Way, Turner, Maine 04282

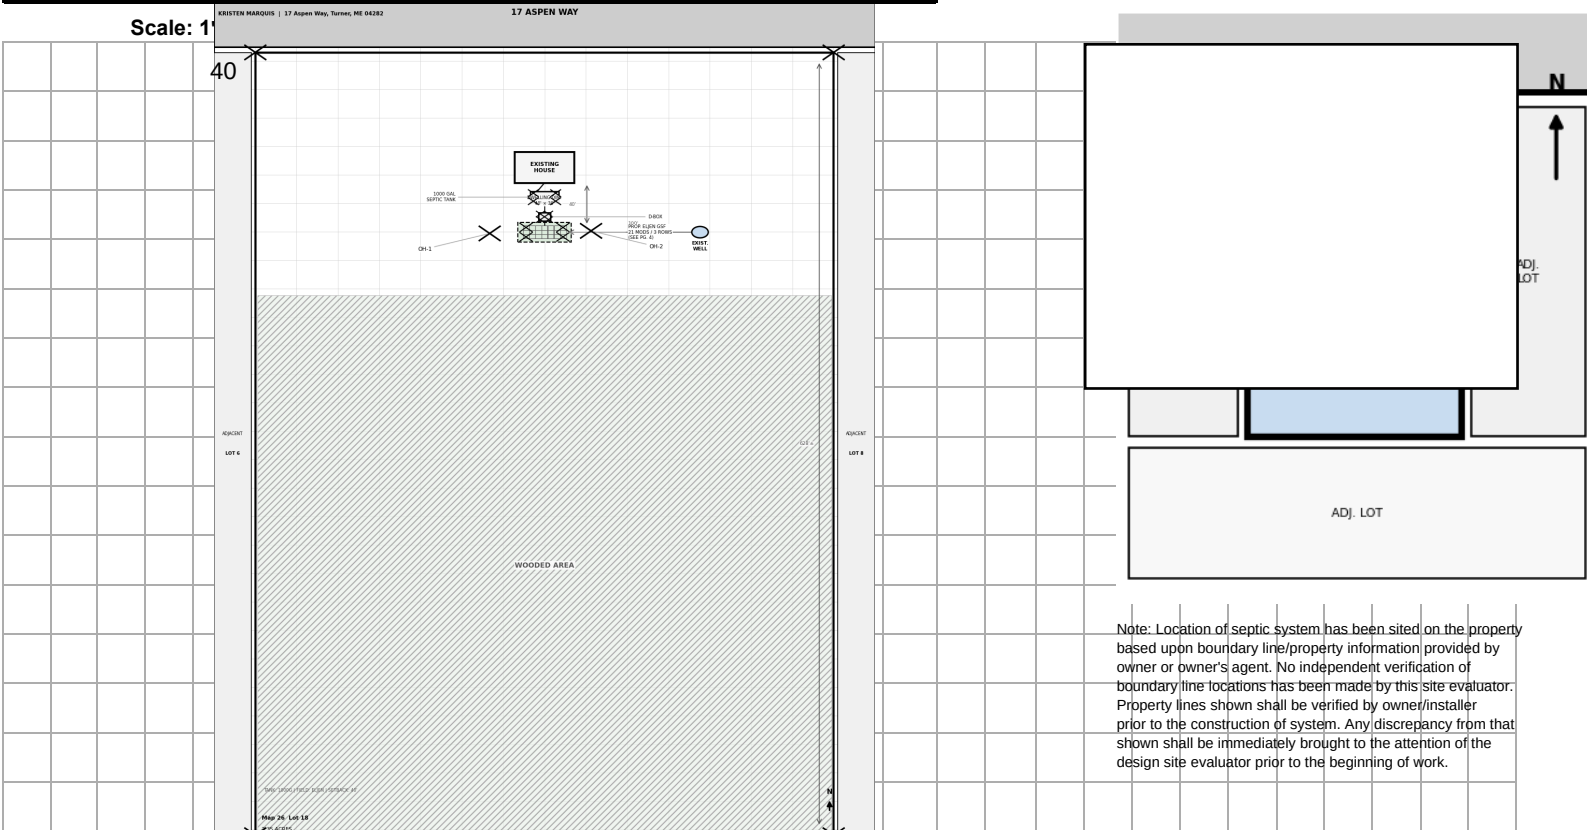

Note: Location of septic system has been sited on the property based upon boundary line/property information provided by owner or owner's agent. No independent verification of boundary/line locations has been made by this site evaluator. Property lines shown shall be verified by owner/installer prior to the construction of system. Any discrepancy from that shown shall be immediately brought to the attention of the design site evaluator prior to the beginning of work.

SOIL PROFILE DESCRIPTION AND CLASSIFICATION

(Location of Observation Holes Shown Above)

Observation Hole #

1

Organic Horizon Thickness

0

 "

Test Pit ☐ Boring ☐

Ground Surface Elevation "

Depth to Exploration or Refusal "

SPECIAL NOTE: EXISTING DISPOSAL FIELD, EXISTING BIOMAT, AND A MINIMUM OF 12 INCHES OF EXISTING SOIL BELOW PROPOSED DISPOSAL AREA AND FILL EXTENSIONS SHALL BE REMOVED, WHERE ENCOUNTERED, AND REPLACED WITH SOIL BACKFILL PER SECTION 11(C) OF THE CODE.

Observation Hole #

2

Organic Horizon Thickness

0

 "

Test Pit ☐ Boring ☐

Ground Surface Elevation "

Depth to Exploration or Refusal "

	Textures	Consistence	Color	Redox Features
0	0			
6	0-3 in brown;	yellowish brown	brown	
12	0-24 in yellowish brown;			
18	unknown olive gray			
24				
30				
36				
42				
48				

Soil Classification		Slope	Limiting Factor	☒ Ground water
olive gray		%	"	☒ Restrictive Layer
Profile	Condition			☐ Bedrock
				☐ Pit Depth

	Textures	Consistence	Color	Redox Features
0	0			
6	0-3 in brown;			
12	0-24 in yellowish brown;			
18	unknown olive gray			
24				
30				
36				
42				
48				

Soil Classification		Slope	Limiting Factor	☒ Ground water
olive gra		%	"	☒ Restrictive Layer
Profile	Condition			☐ Bedrock
				☐ Pit Depth

338

3/1/2026

Site Evaluator Signature or InitialsSE #Date

SUBSURFACE WASTEWATER DISPOSAL SYSTEM APPLICATION

Maine DHHS/CDC – Division of Environmental and Community Health
(207) 287-2070 | Fax (207) 287-4172 | subsurface.wastewater@maine.gov

Owner

Kristen Marquis

Address

17 Aspen Way, Turner, Maine 042

Scale 1" = 40

ft.

SUBSURFACE WASTEWATER DISPOSAL PLAN

SINGLE
FAMILY
DWELLING

4" NON-PERF. PIPE

PROP. 1000 GAL SEPTIC TANK

(EXISTING — INSPECT & REPAIR AS REQ'D)

4" DIA NON-PERF. PIPE

NOTES:

1. REFER TO GENERAL NOTES ON THE BACKSIDE OF THIS PAGE
 2. ALL DISTURBED AREAS AND FINISHED SURFACE SHALL BE LOAMED, SEEDED, AND MULCHED TO PREVENT EROSION
 3. SEPTIC TANK SHALL BE SEALED TO PREVENT GROUND WATER OR SURFACE WATER INFILTRATION INTO SYSTEM
 4. PROVIDE SURFACE WATER DRAINAGE (FLOW) AWAY FROM SYSTEM
- MINIMUM SEPARATION DISTANCES:
A) SEPTIC TANK FROM HOUSE 8 FEET
SEPTIC TANK FROM WELL 50 FEET
DISPOSAL FIELD FROM HOUSE 20 FEET
DISPOSAL FIELD FROM WELL 100 FEET

SEPTIC TANK NOTE: EXISTING 1,000 GALLON SEPTIC TANK SHALL BE EXPOSED, PUMPED AND INSPECTED FOR STRUCTURAL INTEGRITY. IF TANK OR BAFFLES ARE DETERIORATED, TANK SHALL BE REPLACED AND/OR NEW PLASTIC BAFFLES INSTALLED AS APPROPRIATE. INSTALL 18" DIA ACCESS RISER PER SECTION 7F(A)(2).

11'

ROW 1
ROW 2
ROW 3

4" Ø PERF. DIST. PIPE

ELJEN GSF-B43 MODULE (TYP.)

41" x 3.7' W

SCALE: 1" = 10'

28'

SETBACK REQUIREMENTS

FIELD TO WELL:	100' MIN
FIELD TO HOUSE:	40' MIN
TANK TO HOUSE:	8' MIN
TOTAL MODULES:	21 ELJEN GSF

Backfill Requirements Above Existing Grade

Depth of Backfill (upslope)

"

Depth of Backfill (downslope)

"

Depth at Cross-Section (shown below)

Construction Elevations from Elevation Reference Point

Finished Grade Elevation

0

Location & Description:

Top of Distribution Pipe or Proprietary Device

-12

0 -12

Bottom of Disposal Field

30

Reference Elevation is: 0.0 " or "

Scales:

1

10

DISPOSAL AREA CROSS SECTION

TOPOGRAPHIC ELEV. REFERENCE POINT (ERP)
TOP PIPE
FINISHED GRADE
BOT. DISPOSAL FLD.

FINISHED GRADE (ERP = 0.0')

CROWN @ 3% SLOPE

SPECIFIED SAND

EXISTING GRADE

4" Ø PERF. DIST. PIPE THRU MODULES (TYP.)

NOTES

- 1) USE ONLY CLEAN "GRAVELLY COARSE SAND" BACKFILL MATERIAL WHICH MEETS THE BACKFILL STANDARDS OF SECTION 10(B) OF THE "RULES" FREE OF FOREIGN MATERIALS (ROOTS, LARGE ROCKS, ETC.) PLACED IN 8" LIFTS AND LIGHTLY COMPACTED AS PLACED.
- 2) REMOVE ALL ORGANIC MATERIALS (ROOTS, STUMPS, AND LARGE ROCKS) UNDER SYSTEM AND FILL EXTENSIONS AND TRANSITION HORIZON BY PLACING A MINIMUM OF 4" OF CLEAN FILL OVER ORIGINAL SOIL AND MIX (BY PLOWING, DISKING OR ROTOTILLING) INTO ORIGINAL SOIL PER SECTION 10(B) OF THE "RULES".
- 3) PLACE "ANTI-SILTATION FABRIC" OVER MODULES AND PERFORATED DISTRIBUTION PIPES TO KEEP FINES OUT OF THE ELJEN GSF MODULES.

XXX DENOTES TRANSITION HORIZON: THE AREA UNDER THE DISPOSAL AREA MUST BE "ROUGHENED" AT LEAST 6" TO 8" DEEP, THEN PLACE A MINIMUM OF 4" OF CLEAN FILL OVER THIS AREA AND MIX (BY PLOWING, DISKING OR ROTOTILLING) INTO ORIGINAL SOIL PER SECTION 10(B) OF THE "RULES".

VERTICAL: 1" = 1' HORIZONTAL: 1" = 5'

Site Evaluator Signature or Initials

SE #

Date

338

3/1/2026