

SUBSURFACE WASTEWATER DISPOSAL SYSTEM APPLICATION

Maine DHHS/CDC - Division of Environmental and Community Health
(207) 287-2070 I Fax (207) 287-4172 I subsurface.wastewater@maine.gov

Owner


KRISTEN MARQUIS

Address

17 ASPEN WAY

Scale: 1"= 10 ft.

SUBSURFACE WASTEWATER DISPOSAL PLAN

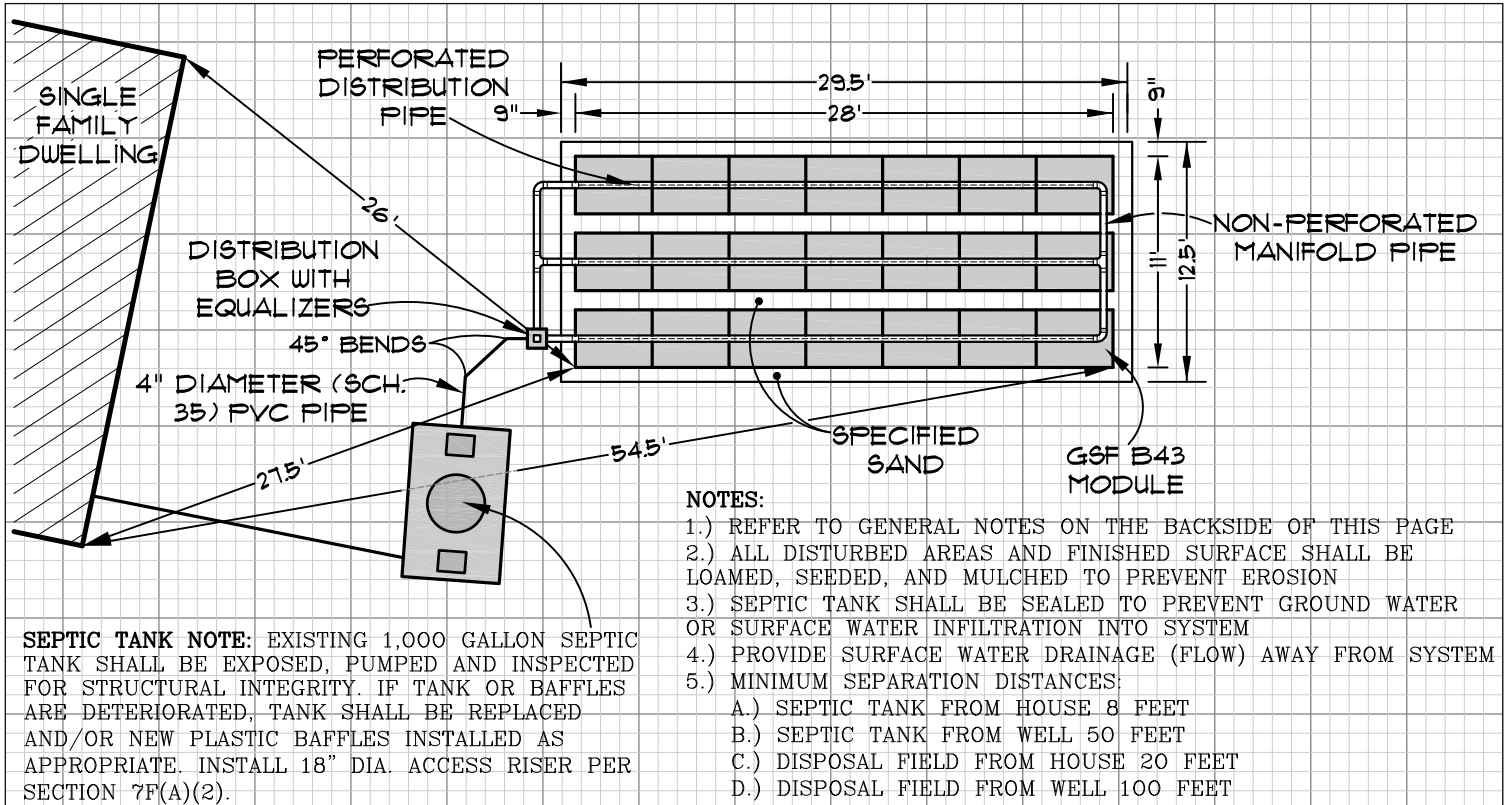

Backfill Requirements Above Existing Grade

Construction Elevations from Elevation Reference Point

Elevation Reference Point


Depth of Backfill (upslope)	12 "
Depth of Backfill (downslope)	32 "
Depths at Cross-Section (shown below)	

Finish Grade (Elevation)	+4 "
Top of Distribution Pipe or Proprietary Device	-14 "
Bottom of Disposal Field	-26 "

Location & Description:	TOP OF EXISTING SEPTIC TANK
Reference Elevation is: 0.0" or	0 "

Scales:
Vertical: 1"= 2.5 ft.
Horizontal: 1"= 5 ft.

DISPOSAL AREA CROSS-SECTION

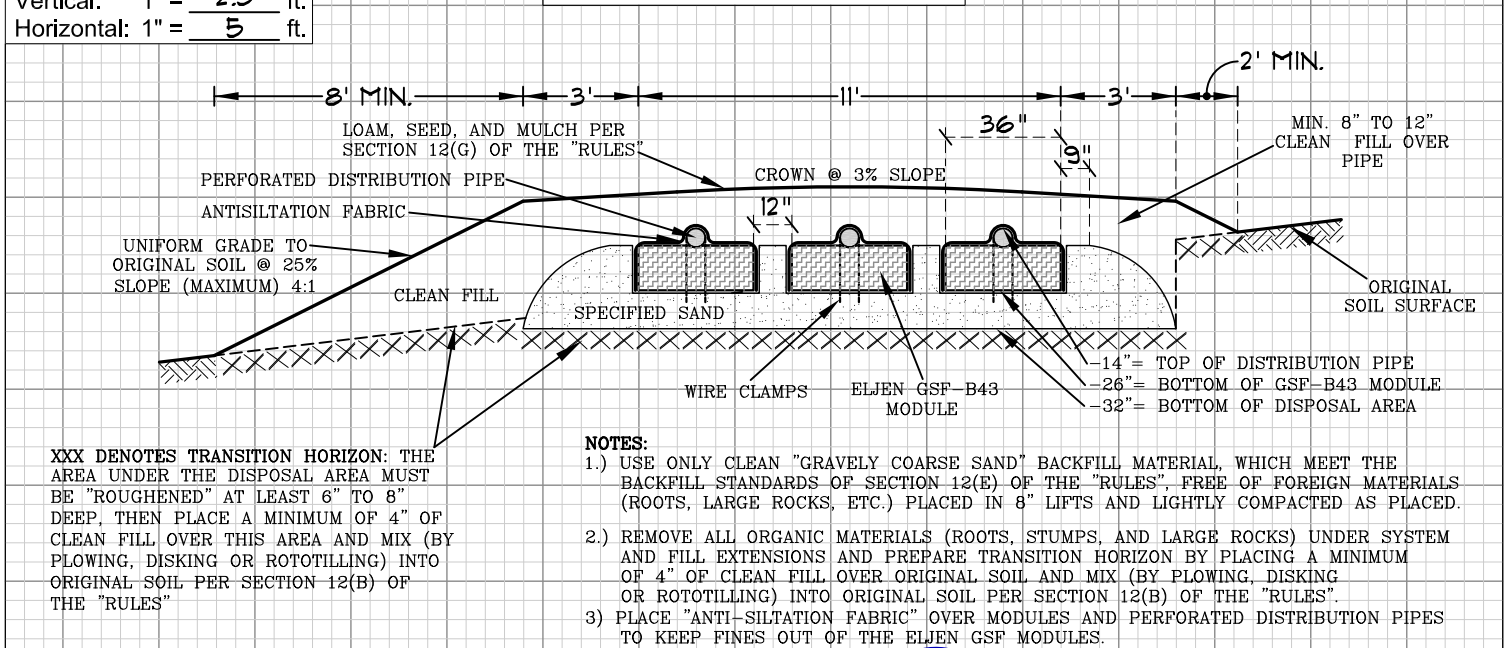

Geary Baerhle
Site Evaluator Signature or Initials

338
SE #

2/20/2026
Date