

# SUBSURFACE WASTEWATER DISPOSAL SYSTEM APPLICATION

Maine DHHS/CDC - Division of Environmental and Community Health  
(207) 287-2070 | Fax (207) 287-4172 | subsurface.wastewater @maine.gov

Owner

CHARLES ROBERTS


Address

450 LANE ROAD

Scale: 1"= 100 ft.

## SITE PLAN

## SITE LOCATION

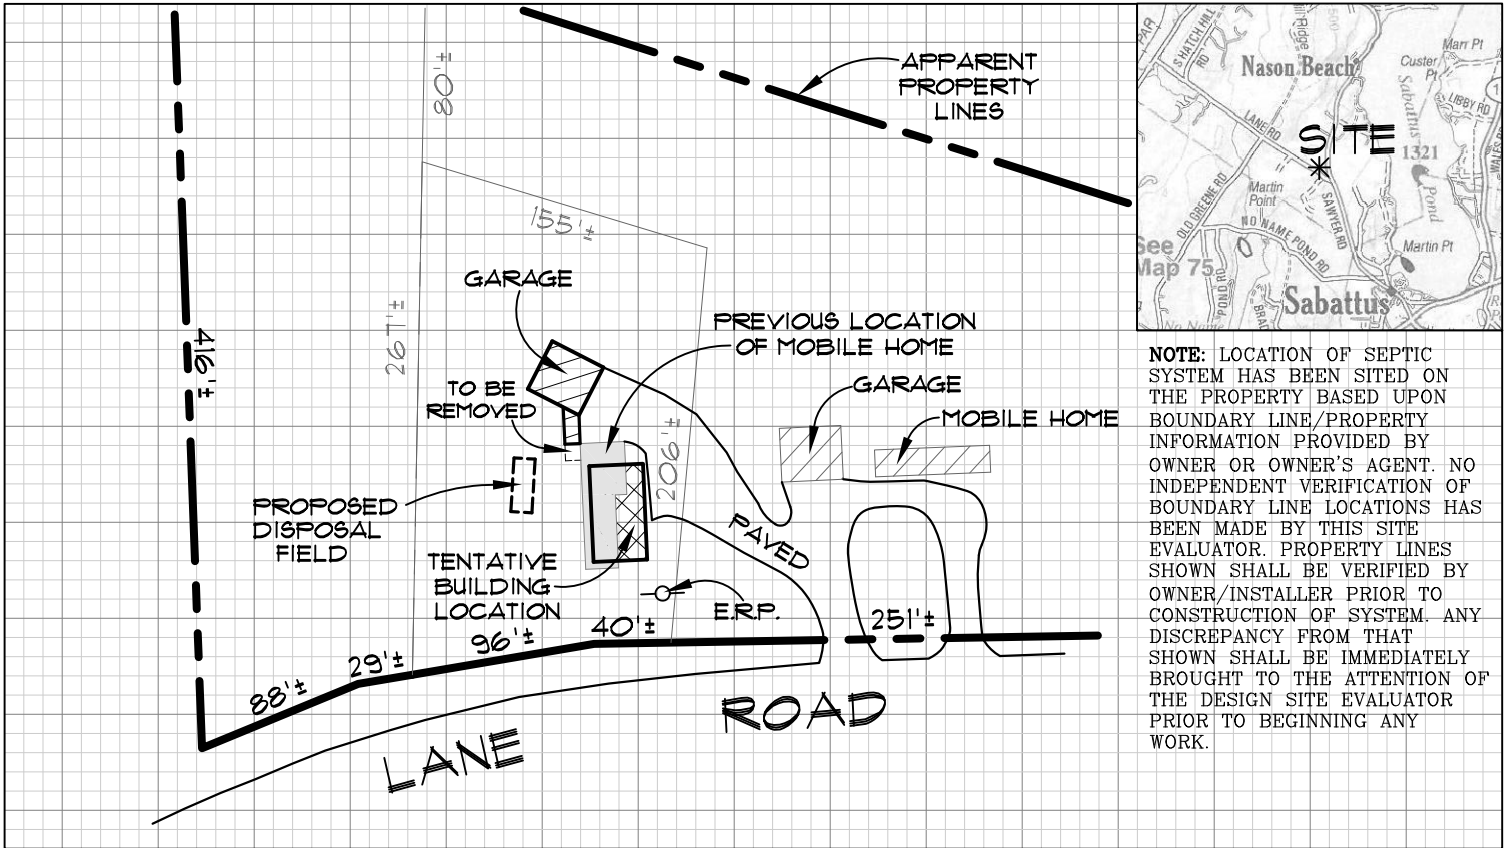

## SOIL PROFILE DESCRIPTION AND CLASSIFICATION

(Location of Observation Holes Shown Above)

Observation Hole #  Organic Horizon Thickness "  
Test Pit ☐ Boring ☐ Ground Surface Elevation "  
Depth to Exploration or Refusal "

Observation Hole #  Organic Horizon Thickness "  
Test Pit ☐ Boring ☐ Ground Surface Elevation "  
Depth to Exploration or Refusal "

|    | Textures | Consistency | Color     | Redox Features |
|----|----------|-------------|-----------|----------------|
| 0  |          |             | BROWN     |                |
| 6  |          |             |           |                |
| 12 | FINE     |             | YELLOWISH |                |
| 18 |          | FRIABLE     |           |                |
| 24 | SANDY    |             | BROWN     |                |
| 30 | LOAM     |             |           |                |
| 36 |          | FIRM        | OLIVE     |                |
| 42 |          |             | GRAY      |                |
| 48 |          |             |           |                |

|    | Textures | Consistency | Color | Redox Features |
|----|----------|-------------|-------|----------------|
| 0  |          |             |       |                |
| 6  |          |             |       |                |
| 12 |          |             |       |                |
| 18 |          |             |       |                |
| 24 |          |             |       |                |
| 30 |          |             |       |                |
| 36 |          |             |       |                |
| 42 |          |             |       |                |
| 48 |          |             |       |                |

**SPECIAL NOTE:** EXISTING DISPOSAL FIELD, EXISTING BIOMATT AND A MINIMUM OF 6 INCHES OF EXISTING SOIL BELOW PROPOSED DISPOSAL AREA AND FILL EXTENSIONS SHALL BE REMOVED, WHERE ENCOUNTERED, AND REPLACED WITH SUITABLE SOIL BACKFILL PER SECTION 12(E) OF THE CODE.

*Gary Baerle*

Site Evaluator Signature or Initials

338

SE #

6/11/2026

Date