

# SUBSURFACE WASTEWATER DISPOSAL SYSTEM PERMIT APPLICATION

Maine CDC: Drinking Water Program  
Attn: SSWW Unit  
286 Water Street, 3<sup>rd</sup> floor  
Augusta, ME 04330

| Property Address      |  |       |  |
|-----------------------|--|-------|--|
| Address (# & Street)  |  |       |  |
| City/Town/ Plantation |  |       |  |
| Municipal Tax Map #   |  | Lot # |  |

| Property Owner or Applicant Information |  |
|-----------------------------------------|--|
| Owner Name (Last, First)                |  |
| Applicant Name                          |  |

| Owner or Applicant Mailing Address |  |       |     |
|------------------------------------|--|-------|-----|
| Street                             |  |       |     |
| City                               |  | State | Zip |
| Phone                              |  |       |     |
| Email                              |  |       |     |

| Owner/ Applicant Statement   |      |
|---|------|
| I certify that the information submitted is correct to the best of my knowledge and understand that any falsification is reason for the Department and/or Local Plumbing Inspector(s) to deny a permit. |      |
| X   |      |
| Property Owner/ Applicant Signature   | Date |

| Installer Information |       |
|-----------------------|-------|
| Name                  | Phone |
| Email                 |       |

| Issuing Municipality or Territory |             |
|-----------------------------------|-------------|
| Permit #                          | Date Issued |
| X                                 |             |

Local Plumbing Inspector Signature LPI #

A subsurface wastewater disposal system may not be installed until a permit is issued by the Local Plumbing Inspector. The permit authorizes the installation of the disposal system in accordance with 10-144-CMR Chapter 241.

## CAUTION: INSPECTION REQUIRED

"I have inspected the installation authorized above and found it to be in compliance with the Subsurface Wastewater Disposal Rules Application."

|   |  |
|---|--|
| X |  |
|---|--|

Local Plumbing Inspector Signature Date

|   |  |
|---|--|
| X |  |
|---|--|

Local Plumbing Inspector Signature Date

| Fee Calculations (For Town/ LPI Use Only) |    |
|-------------------------------------------|----|
| <input type="checkbox"/> Revision         |    |
| <input type="checkbox"/> Doubled Fee      |    |
| <input type="checkbox"/> Variance         |    |
| <input type="checkbox"/> Seas. Conv.      |    |
| Total Fee                                 | \$ |
| Town Share                                | \$ |
| State 25%                                 | \$ |
| DEP WQS                                   | \$ |

The Town retains all doubled fees  
The State receives 25% for First-time variances requiring State approval *only*  
Seas. Conv. must be a stand-alone permit

| Type of Application                                    | Variance Requirements                           |
|--------------------------------------------------------|-------------------------------------------------|
| <input type="checkbox"/> 1. First Time System          | <input type="checkbox"/> 1. No Rule Variance    |
| <input type="checkbox"/> 2. Replacement System         | <input type="checkbox"/> 2. First Time System   |
| Type Replaced                                          | LPI Only <input type="checkbox"/>               |
| Year Installed                                         | State Required <input type="checkbox"/>         |
| <input type="checkbox"/> 3. Expansion                  | <input type="checkbox"/> 3. Replacement System  |
| <input type="checkbox"/> <25% (Minor) Expansion        | LPI Only <input type="checkbox"/>               |
| <input type="checkbox"/> ≥25% (Major) Expansion        | State Required <input type="checkbox"/>         |
| <input type="checkbox"/> 4. Experimental System        | <input type="checkbox"/> 4. Minimum Lot Size    |
| <input type="checkbox"/> 5. Seasonal Conversion Permit | <input type="checkbox"/> 5. Seasonal Conversion |

| Treatment Tank(s)                                       |   |
|---------------------------------------------------------|---|
| <input type="checkbox"/> 1. Concrete                    | <input type="checkbox"/> Regular <input type="checkbox"/> Low Profile <input type="checkbox"/> H-20 |
| <input type="checkbox"/> 2. Plastic                     |   |
| <input type="checkbox"/> 3. External Grease Interceptor | Capacity                                                                                            |
| <input type="checkbox"/> 4. Other                       | Specify                                                                                             |
| Tank Capacity                                           | gals                                                                                                |
| Total # of New Tanks                                    |   |

Notes:

☐ Riser(s) required in accordance with 10-144-CMR Chapter 241 (7)(F)(2)(a)

| Disposal System Components                                                             |                        |
|----------------------------------------------------------------------------------------|------------------------|
| <input type="checkbox"/> 1. Complete Non-Engineered System                             | (Field /Tank /Pump)    |
| Specify Total Number of New Tanks                                                      |                        |
| <input type="checkbox"/> 2. Primitive/ Limited System (Greywater + Alternative Toilet) |                        |
| Specify Type                                                                           |                        |
| <input type="checkbox"/> 3. Alternative Toilet                                         |                        |
| Specify Type                                                                           |                        |
| <input type="checkbox"/> 4. Non-Engineered Treatment Tank(s)                           | (750 gals or over*)    |
| Specify Total # of New Tanks:                                                          |                        |
| <input type="checkbox"/> 5. Holding Tank                                               |                        |
| <input type="checkbox"/> 6. Non-Engineered Disposal Field                              |                        |
| <input type="checkbox"/> 7. Complete Engineered System                                 | (Field/ 2 Tanks/ Pump) |
| New: # Disposal Fields # Tanks # Pumps                                                 |                        |
| <input type="checkbox"/> 8. Engineered Tank(s) Only                                    | Specify # of New Tanks |
| <input type="checkbox"/> 9. Engineered Field(s) Only                                   |                        |
| <input type="checkbox"/> 10. Miscellaneous Components                                  | Specify                |
| <input type="checkbox"/> 11. Pre-Treatment Tank (Tank fees apply)**                    |                        |
| <input type="checkbox"/> 12. Pre-Treatment Component (Misc. Component fees apply)**    |                        |

\*Includes Grease Interceptors, Pump Tanks, etc. \*\*Details on Pg. 2

## Site Evaluator Statement

I certify that I have completed a site evaluation on this property and state that the data reported are accurate and that the proposed system is in compliance with the State of Maine Subsurface Wastewater Disposal Rules (10-144A CMR 241).

|                             |       |       |
|-----------------------------|-------|-------|
| Site Evaluator Name (Print) | Phone | SE #  |
| Signature                   | Date  | Email |

**SUBSURFACE WASTEWATER DISPOSAL SYSTEM APPLICATION**Maine DHHS/CDC – Division of Environmental and Community Health  
(207) 287-2070 | Fax (207) 287-4172 | subsurface.wastewater@maine.gov

Owner

Address

**Property Size** ☐ sq. ft. ☐ acres**Shoreland Zoning**☐ Yes**Current Use**☐ Seasonal ☐ Undeveloped  
☐ No ☐ Year-Round ☐ Commercial**Latitude & Longitude (D.M.S.)**Latitude   
Longitude 

GPS margin of error

**Type of Water Supply**☐ 1. Drilled Well ☐ 2. Dug/ Point Well  
☐ 3. Private ☐ 4. Public ☐ 5. Other

Specify:

**Effluent/ Ejector Pump**Required: ☐ Yes ☐ No ☐ MaybeDose (Engineered Systems)  gals**Garbage Disposal Unit**☐ Yes ☐ No ☐ Maybe *If Yes...*☐ Multi-compartment Tank  
☐ Tanks in Series # of Tanks   
☐ Increase Tank Capacity  
☐ Filter on Tank Outlet**Pre-/ Advanced Treatment Systems**

Make

Model

Notes:

☐ Maintenance contract (HHE-300A) required

Make

Model

Notes:

☐ Maintenance contract (HHE-300A) required**Disposal System to Serve**☐ 1. Single Family Dwelling Unit# of bedrooms: ☐ 2. Multiple Family Dwelling Units# of bedrooms: ☐ 3. Accessory Dwelling Unit(s)# of bedrooms: ☐ 4. Other

Specify:

**Disposal Field Type & Size**☐ 1. Stone Bed  
☐ 2. Stone Trench  
☐ 3. Proprietary Device  
☐ Cluster Array ☐ Linear  
☐ Regular ☐ Load  
☐ 4. Other

Specify:

Size  ☐ sq. ft. ☐ lin. ft.**Design Flow** Gallons per Day*Based on (select one)*☐ 1. Table 5A (Dwelling Units)  
☐ 2. Table 5C (Other Facilities)

Show Calculations for "Other Facilities"

☐ 3. Section 5(G) – Meter Readings

ATTACH WATER METER DATA

**Soil Data & Design Class**

Profile

Condition

At Observation Hole # 

Limiting Factor Depth

Limiting Factor Elevation

Highest Elevation within Disposal Field

**Additional Notes**

Site Evaluator Signature or Initials

SE #


Date

SUBSURFACE WASTEWATER DISPOSAL SYSTEM APPLICATION

Maine DHHS/CDC – Division of Environmental and Community Health  
(207) 287-2070 | Fax (207) 287-4172 | subsurface.wastewater@maine.gov

Owner

Address

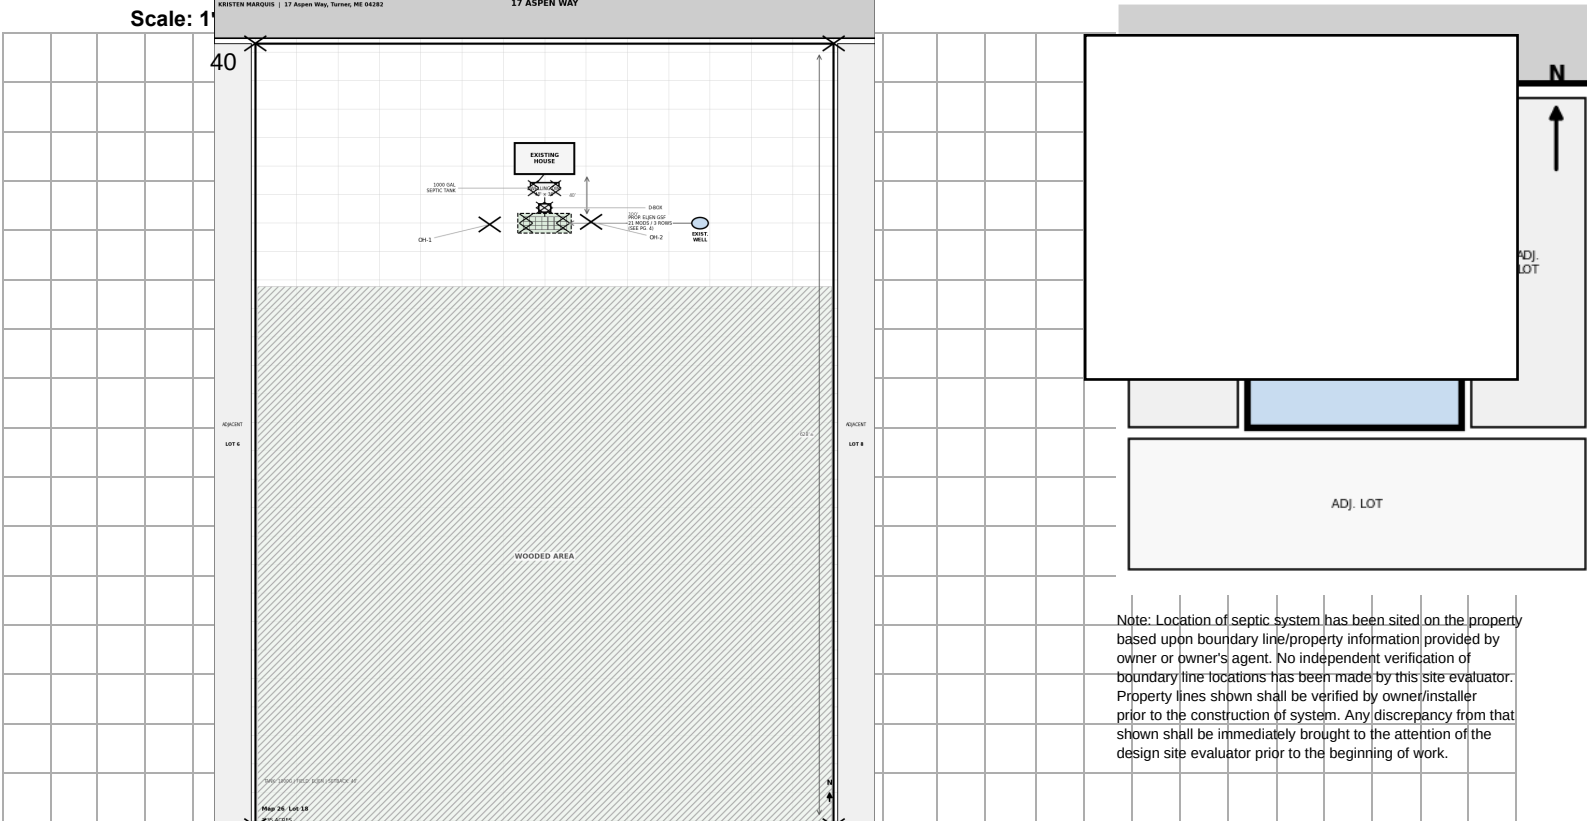

SOIL PROFILE DESCRIPTION AND CLASSIFICATION

(Location of Observation Holes Shown Above)

Observation Hole #

Organic Horizon Thickness

Test Pit Boring

Ground Surface Elevation

Depth to Exploration or Refusal

SPECIAL NOTE: EXISTING DISPOSAL FIELD, EXISTING BIOMATT AND A MINIMUM OF 12 INCHES OF EXISTING SOIL BELOW PROPOSED DISPOSAL AREA AND FILL EXTENSIONS SHALL BE REMOVED, WHERE ENCOUNTERED, AND REPLACED WITH SOIL BACKFILL PER SECTION 11(C) OF THE CODE.

Observation Hole #

Organic Horizon Thickness

Test Pit Boring

Ground Surface Elevation

Depth to Exploration or Refusal

|    | Textures | Consistence | Color | Redox Features |
|----|----------|-------------|-------|----------------|
| 0  |          |             |       |                |
| 6  |          |             |       |                |
| 12 |          |             |       |                |
| 18 |          |             |       |                |
| 24 |          |             |       |                |
| 30 |          |             |       |                |
| 36 |          |             |       |                |
| 42 |          |             |       |                |
| 48 |          |             |       |                |

|    | Textures | Consistence | Color | Redox Features |
|----|----------|-------------|-------|----------------|
| 0  |          |             |       |                |
| 6  |          |             |       |                |
| 12 |          |             |       |                |
| 18 |          |             |       |                |
| 24 |          |             |       |                |
| 30 |          |             |       |                |
| 36 |          |             |       |                |
| 42 |          |             |       |                |
| 48 |          |             |       |                |

| Soil Classification |           | Slope | Limiting Factor | <div><input type="checkbox"/> Ground water</div> <div><input type="checkbox"/> Restrictive Layer</div> <div><input type="checkbox"/> Bedrock</div> <div><input type="checkbox"/> Pit Depth</div> |
|---------------------|-----------|-------|-----------------|---|
|                     |           | %     | "               |   |
| Profile             | Condition |       |                 |   |

| Soil Classification |           | Slope | Limiting Factor | <input type="checkbox"/> Ground water      |
|---------------------|-----------|-------|-----------------|--------------------------------------------|
|                     |           | %     | "               | <input type="checkbox"/> Restrictive Layer |
| Profile             | Condition |       |                 | <input type="checkbox"/> Bedrock           |
|                     |           |       |                 | <input type="checkbox"/> Pit Depth         |

Site Evaluator Signature or Initials

SE #

Date

# SUBSURFACE WASTEWATER DISPOSAL SYSTEM APPLICATION

Maine DHHS/CDC – Division of Environmental and Community Health  
(207) 287-2070 | Fax (207) 287-4172 | subsurface.wastewater@maine.gov

Owner

Address

Scale 1" =

ft.

## SUBSURFACE WASTEWATER DISPOSAL PLAN

SINGLE FAMILY DWELLING

4" NON-PERF. PIPE

PROP. 1000 GAL SEPTIC TANK

(EXISTING — INSPECT & REPAIR AS REQ'D)

4" DIA NON-PERF. PIPE

### NOTES:

1. REFER TO GENERAL NOTES ON THE BACKSIDE OF THIS PAGE
  2. ALL DISTURBED AREAS AND FINISHED SURFACE SHALL BE LOAMED, SEEDED, AND MULCHED TO PREVENT EROSION
  3. SEPTIC TANK SHALL BE SEALED TO PREVENT GROUND WATER OR SURFACE WATER INFILTRATION INTO SYSTEM
  4. PROVIDE SURFACE WATER DRAINAGE (FLOW) AWAY FROM SYSTEM
- MINIMUM SEPARATION DISTANCES:  
A) SEPTIC TANK FROM HOUSE 8 FEET  
SEPTIC TANK FROM WELL 50 FEET  
DISPOSAL FIELD FROM HOUSE 20 FEET  
DISPOSAL FIELD FROM WELL 100 FEET

SEPTIC TANK NOTE: EXISTING 1,000 GALLON SEPTIC TANK SHALL BE EXPOSED, PUMPED AND INSPECTED FOR STRUCTURAL INTEGRITY. IF TANK OR BAFFLES ARE DETERIORATED, TANK SHALL BE REPLACED AND/OR NEW PLASTIC BAFFLES INSTALLED AS APPROPRIATE. INSTALL 18" DIA ACCESS RISER PER SECTION 7F(A)(2).

11'

ROW 1  
ROW 2  
ROW 3

4" Ø PERF. DIST. PIPE

ELJEN GSF-B43 MODULE (TYP.)

41" x 3.7' W

SCALE: 1" = 10'

| SETBACK REQUIREMENTS |              |
|----------------------|--------------|
| FIELD TO WELL:       | 100' MIN     |
| FIELD TO HOUSE:      | 40' MIN      |
| TANK TO HOUSE:       | 8' MIN       |
| TOTAL MODULES:       | 21 ELJEN GSF |

### Backfill Requirements Above Existing Grade

Depth of Backfill (upslope)

"

Depth of Backfill (downslope)

"

Depth at Cross-Section (shown below)

### Construction Elevations from Elevation Reference Point

Finished Grade Elevation

Location & Description:

Top of Distribution Pipe or Proprietary Device

"

Bottom of Disposal Field

"

Reference Elevation is: 0.0 " or -12 "

### Scales:

### DISPOSAL AREA CROSS SECTION

| ELEV. REFERENCE POINT (ERP) |      |
|-----------------------------|------|
| TOP PIPE                    | -12" |
| FINISHED GRADE              | 0"   |
| BOT. DISPOSAL FLD.          | -30" |

FINISHED GRADE (ERP = 0.0')

CROWN @ 3% SLOPE

SPECIFIED SAND

EXISTING GRADE

4" Ø PERF. DIST. PIPE THRU MODULES (TYP.)

### NOTES

- 1) USE ONLY CLEAN "GRAVELLY COARSE SAND" BACKFILL MATERIAL WHICH MEETS THE BACKFILL STANDARDS OF SECTION 10(B) OF THE "RULES" FREE OF FOREIGN MATERIALS (ROOTS, LARGE ROCKS, ETC.) PLACED IN 8" LIFTS AND LIGHTLY COMPACTED AS PLACED.
- 2) REMOVE ALL ORGANIC MATERIALS (ROOTS, STUMPS, AND LARGE ROCKS) UNDER SYSTEM AND FILL EXTENSIONS AND TRANSITION HORIZON BY PLACING A MINIMUM OF 4" OF CLEAN FILL OVER ORIGINAL SOIL AND MIX (BY PLOWING, DISKING OR ROTOTILLING) INTO ORIGINAL SOIL PER SECTION 10(B) OF THE "RULES".
- 3) PLACE "ANTI-SILTATION FABRIC" OVER MODULES AND PERFORATED DISTRIBUTION PIPES TO KEEP FINES OUT OF THE ELJEN GSF MODULES.

XXX DENOTES TRANSITION HORIZON: THE AREA UNDER THE DISPOSAL AREA MUST BE "ROUGHENED" AT LEAST 6" TO 8" DEEP, THEN PLACE A MINIMUM OF 4" OF CLEAN FILL OVER THIS AREA AND MIX (BY PLOWING, DISKING OR ROTOTILLING) INTO ORIGINAL SOIL PER SECTION 10(B) OF THE "RULES".

VERTICAL: 1" = 1' HORIZONTAL: 1" = 5'

Site Evaluator Signature or Initials

SE #

Date